

Vorentwurf Wochenendhaus - Flurstück 7348

Bauvorhaben	Neubau eines Wochenendhauses in Holzbauweise mit Terrasse und einem offenen Stellplatz
Grundstück	Grenzweg 12, 69245 Bammental · Gemarkung Bammental · Flurstück 7348
Planungsrecht	Bebauungsplan „Wochenendhausgebiet – 1. Änderung (Neufassung)“ der Gemeinde Bammental, rechtskräftig 19.09.2008 (Plan Nr. BP 0806, Büro Piske) · SO Wochenendhaus · GRmax 65 m² · I · o
Ziel dieser Unterlage	Vorabstimmung mit der Gemeinde Bammental (Bauamt / Gemeinderat) und der unteren Baurechtsbehörde (Rhein-Neckar-Kreis) vor Einreichung eines Bauantrags. Die Unterlage ist ein Vorentwurf, kein Bauantrag.
Entwurfsidee	Ein einfacher, ruhiger Holzkörper mit steilem Satteldach – die Archetyp-Form der Wochenendhäuser im Gebiet, zeitgemäß interpretiert: unbehandelte Lärchenschalung, die silbergrau vergraut und im Waldrand zurücktritt; anthrazitfarbenes Stehfalzdach; eine große Verglasung zur Wiese nach Süden, geschützt durch einen hölzernen Schiebeladen; eine niedrige Holzterrasse, die das Haus in die Wiese legt. Das Gebäude steht auf Punktfundamenten – der Boden bleibt weitgehend unversiegelt, der Baumbestand außerhalb des Baufensters bleibt erhalten.
Varianten	A – Bebauung exakt im Baufenster 7,20 × 5,20 m (37,44 m²), regelkonform, ohne Befreiung. B – Wunschvariante 8,40 × 6,80 m (57,12 m²) innerhalb der zulässigen GR von 65 m², jedoch mit Überschreitung der Baugrenze → Antrag auf Befreiung nach § 31 Abs. 2 BauGB (Begründung im Erläuterungsbericht).
Inhalt	Blatt 1 Deckblatt · Blatt 2 Lageplan · Blatt 3–6 Variante A (Grundriss, Ansichten, Schnitt, Isometrie) · Blatt 7–10 Variante B · Blatt 11 Nachweis Festsetzungen · Blatt 12 Gestaltung & Material
Bauherr / Verfasser	Bauherr: Fam. Schneider · Vorentwurf erstellt zur Abstimmung; Werkplanung, Statik, Wärmeschutz und amtlicher Lageplan folgen im Bauantrag durch bauvorlageberechtigte Entwurfsverfasser.

Neubau eines Wochenendhauses

Grenzweg 12 · 69245 Bammental · Flurstück 7348


B-Plan „Wochenendhausgebiet – 1. Änderung (Neufassung)“, Gemeinde Bammental, 11.09.2008

Vorentwurf Wochenendhaus - Flurstück 7348

VORENTWURF · Stand 09/2026 · zur Vorabstimmung mit der Gemeinde

Lageplan (schematisch)

Grundstücksgrenzen näherungsweise aus dem B-Plan abgegriffen – für den Bauantrag durch amtlichen Lageplan (Vermesser) zu ersetzen. Nord = oben.

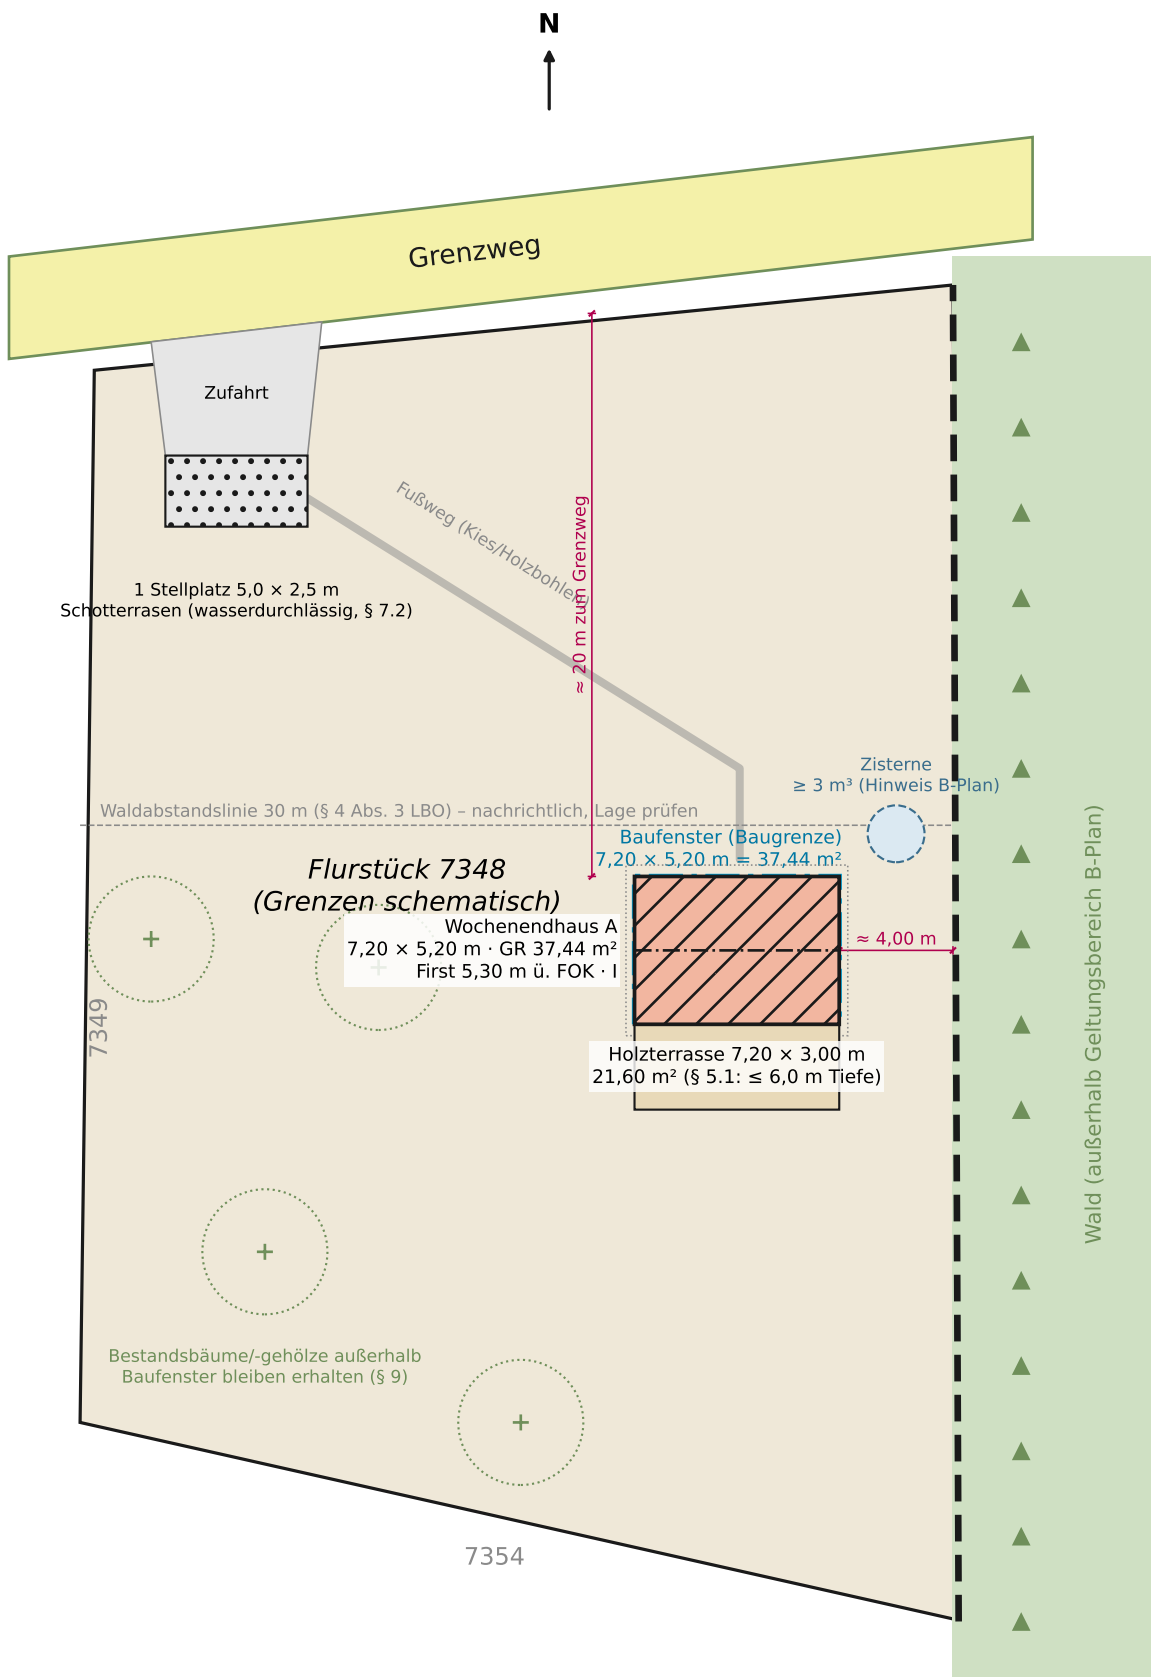

Legende

- Baugrenze (Baufenster) gem. B-Plan
- Wochenendhaus (Neubau), Hauptgebäude
- Dachüberstand (Traufe 0,40 m / Ortgang 0,30 m)
- Holzterrasse, aufgeständert, unüberdacht
- Stellplatz / Zufahrt, wasserdurchlässig
- Grenze Geltungsbereich B-Plan / Waldrand

Flächenbilanz (Variante A)

Grundfläche Hauptgebäude GR 37,44 m² (max. 65 m²)

Terrasse 21,60 m² · Stellplatz+Zufahrt ca. 25 m²

Summe versiegelt/Nebenanlagen ca. 84,04 m²

GRZ bei 900 m² Grundstück: 0,09 (zul. 0,15 inkl. Nebenanlagen)

Hinweise

- Grundstücksfläche lt. Kataster eintragen (Mindestgröße 900 m²).
- Ausrichtung Baufenster / Grenzen vor Ort einmessen lassen.
- Waldabstand: Befreiung/Ausnahme nach § 4 Abs. 3 LBO BW i. V. m.
Forstbehörde – Baufenster liegt lt. B-Plan bereits im 30-m-Streifen.

Neubau eines Wochenendhauses

Grenzweg 12 · 69245 Bammental · Flurstück 7348

B-Plan „Wochenendhausgebiet – 1. Änderung (Neufassung)“, Gemeinde Bammental, 11.09.2008


Lageplan (schematisch)

VORENTWURF · Stand 09/2026 · zur Vorabstimmung mit der Gemeinde

M 1:250 (schematisch)

Grundriss Erdgeschoss - Variante A - Bebauung im Baufenster (Regelfall)

Holzrahmenbau, Außenwand 30 cm (inkl. Lärchenschalung), Innenwände 10 cm. Maße in m. Süden = unten (Terrassenseite).

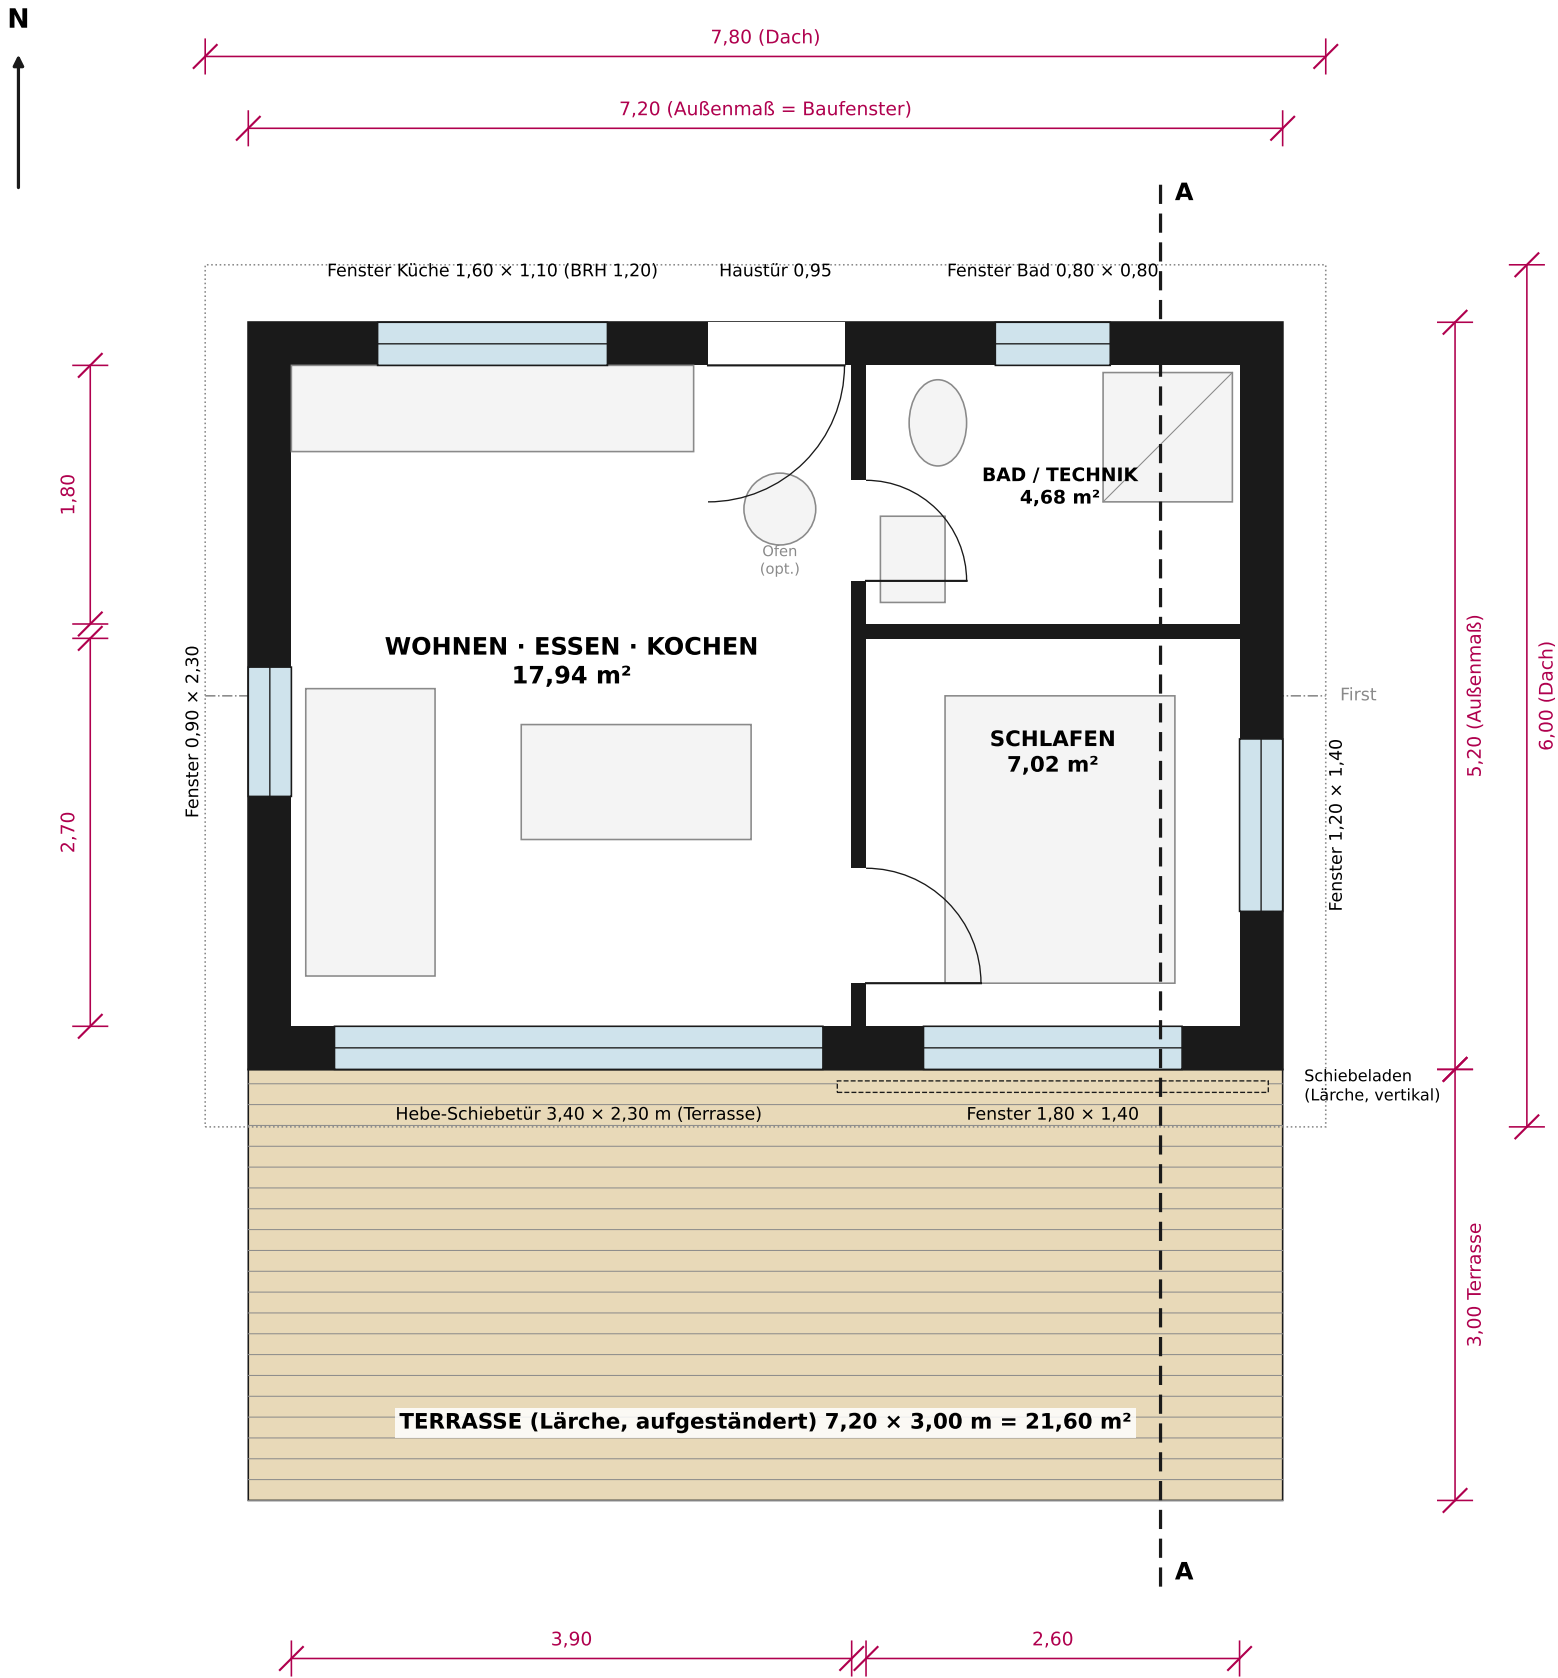

Raumprogramm

Wohnen / Essen / Kochen	17,94 m²
Schlafen	7,02 m²
Bad / WC / Technik	4,68 m²
Wohnfläche EG netto	29,64 m²
Schlafempore (optional, kein Vollgeschoss)	≈ 11,96 m²
Terrasse (unüberdacht)	21,60 m²

Kennwerte

Grundfläche GR (Außenmaß)	37,44 m²
Baufenster lt. B-Plan	37,44 m²
GR max. lt. Nutzungsschablone	65,00 m²
Vollgeschosse	I
Bauweise	offen (o)
Traufhöhe (Schnittpunkt Wand/Dach) ü. FOK	2,70 m
Firsthöhe ü. FOK EG (max. 5,50)	5,30 m
Dachneigung / Dachform	45° Satteldach
Dachüberstand Traufe (max. 0,80)	0,40 m
Dachüberstand Ortgang (0,20–0,60)	0,30 m
FOK EG über Gelände (bergs. ≤0,20 / tals. ≤0,80)	≈ 0,20–0,30 m

Konstruktion

- Holzrahmenbau, vorgefertigt, diffusionsoffen
- Fassade: Lärche sägerau, horizontal, unbehandelt
- Dach: Stehfalz, beschichtetes Blech (kein Cu/Zn/Pb blank)
- Gründung: Punkt-/Schraubfundamente (minimaler Eingriff)

Neubau eines Wochenendhauses

Grenzweg 12 · 69245 Bammental · Flurstück 7348
B-Plan „Wochenendhausgebiet – 1. Änderung (Neufassung)“, Gemeinde Bammental, 11.09.2008

Grundriss EG - Variante A

VORENTWURF · Stand 09/2026 · zur Vorabstimmung mit der Gemeinde


M 1:50

Blatt 3


Ansichten - Variante A - Bebauung im Baufenster (Regelfall)

Fassade Lärche horizontal (vergraut), Dach Stehfalz anthrazit (beschichtet), Fenster Holz-Alu. Höhen in m bezogen auf FOK EG = ±0,00.


Ansicht Süd (Terrasse / Gartenseite)

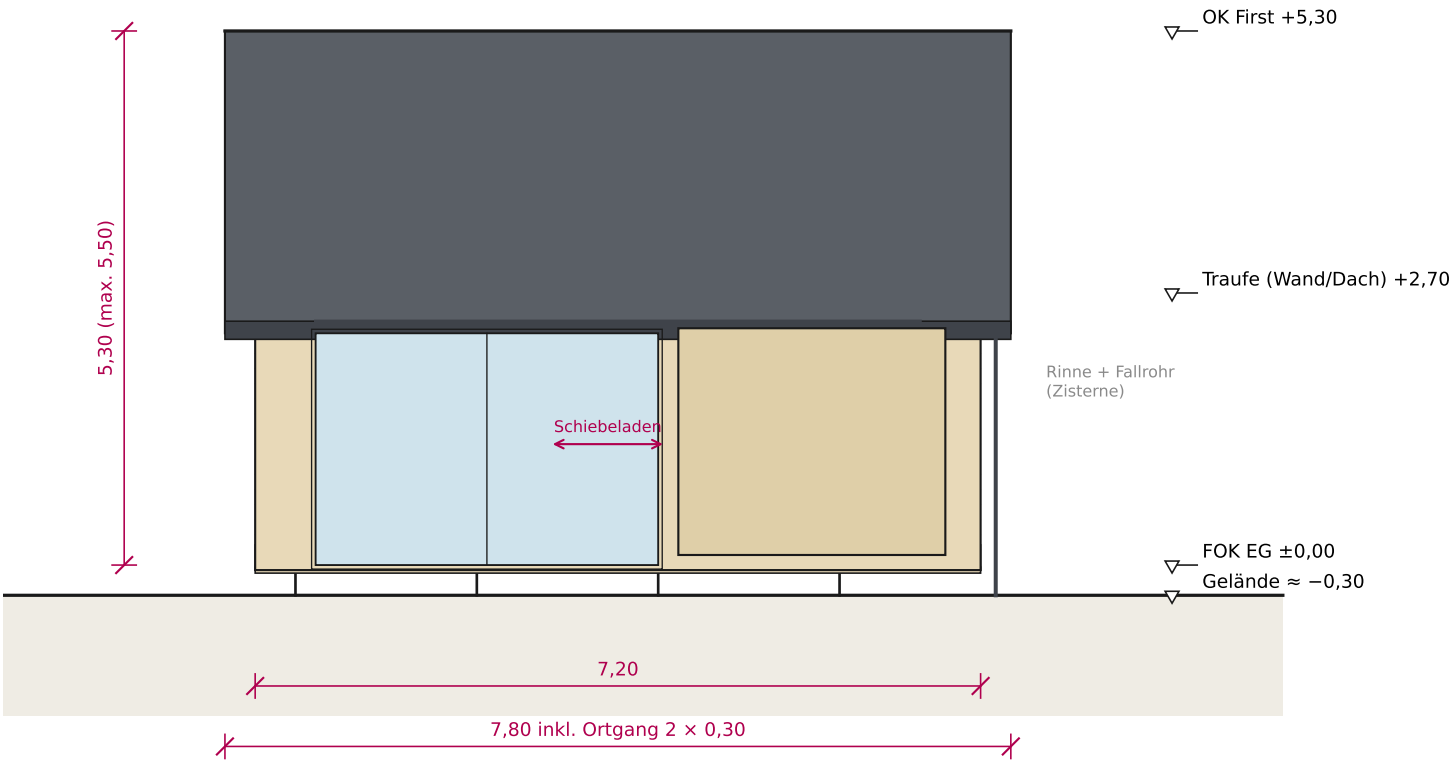


Ansicht Nord (Eingang / Grenzweg)

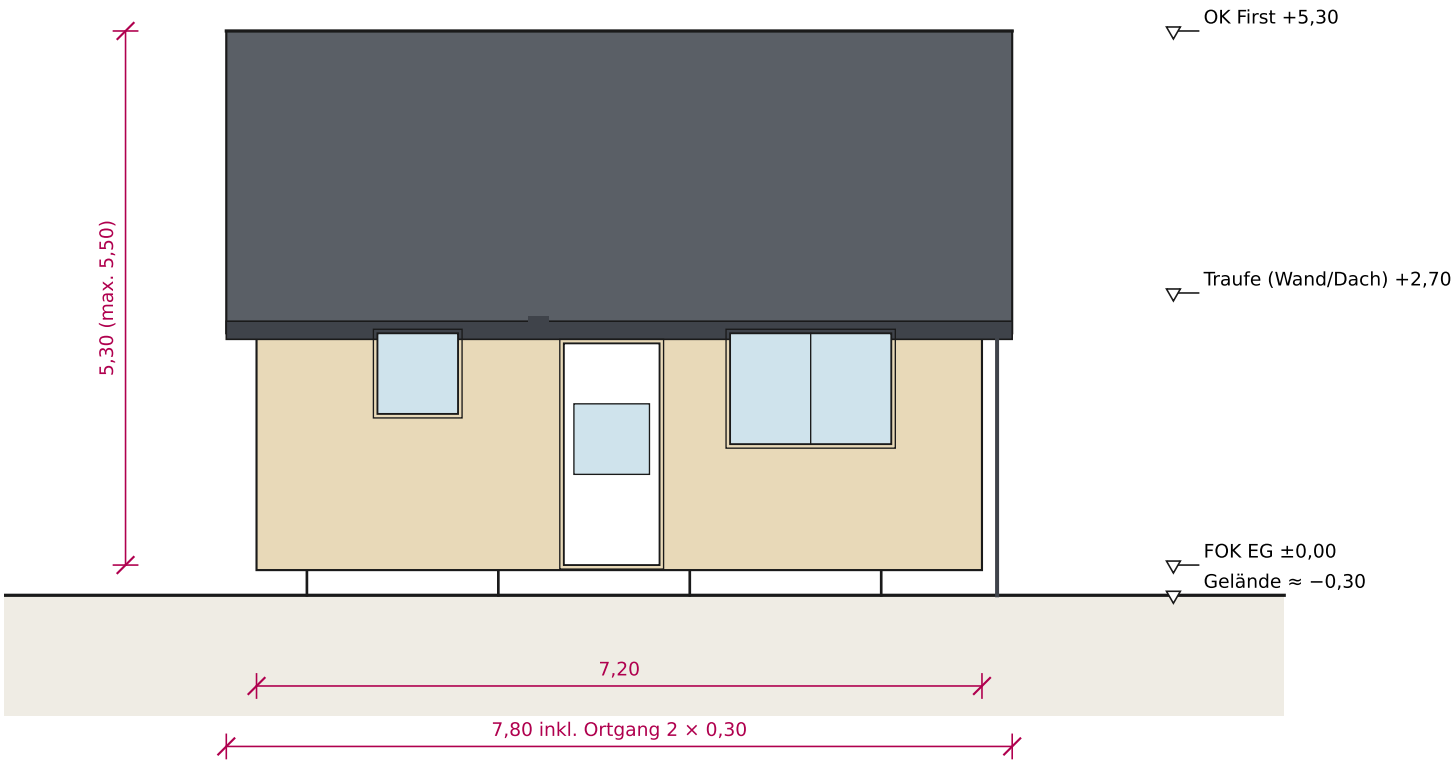

Ansicht Ost (Giebel, Waldseite)

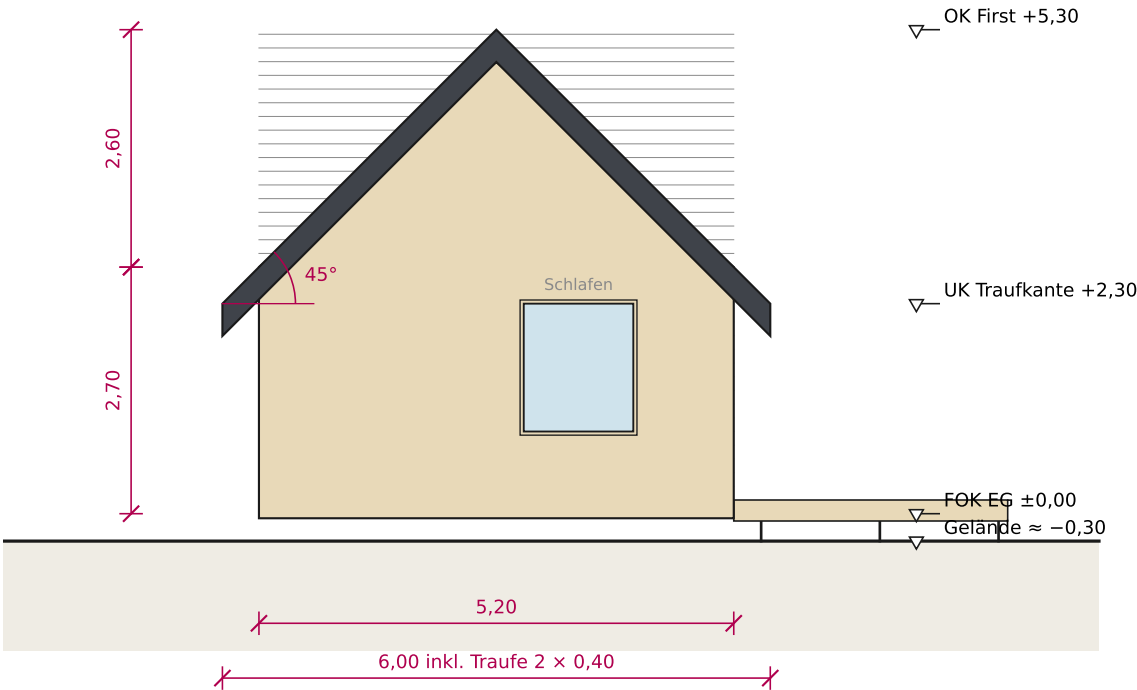

Ansicht West (Giebel)

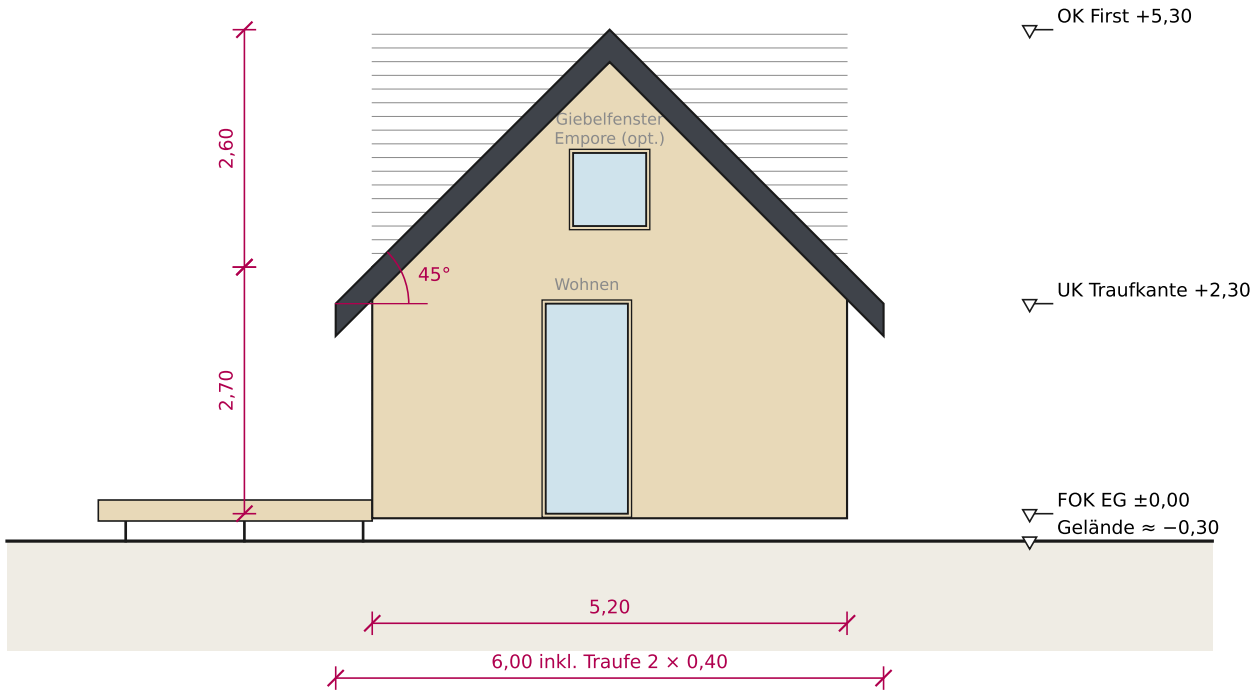

Neubau eines Wochenendhauses

Grenzweg 12 · 69245 Bammental · Flurstück 7348

B-Plan „Wochenendhausgebiet – 1. Änderung (Neufassung)“, Gemeinde Bammental, 11.09.2008

Ansichten - Variante A


VORENTWURF · Stand 09/2026 · zur Vorabstimmung mit der Gemeinde

M 1:100

Blatt 4

Schnitt A-A - Variante A - Bebauung im Baufenster (Regelfall)

Schnitt durch Schlaf-/Badzone mit optionaler Schlafempore (kein Vollgeschoss: lichte Höhe ≥ 2,30 m auf deutlich < 3/4 der Grundfläche).

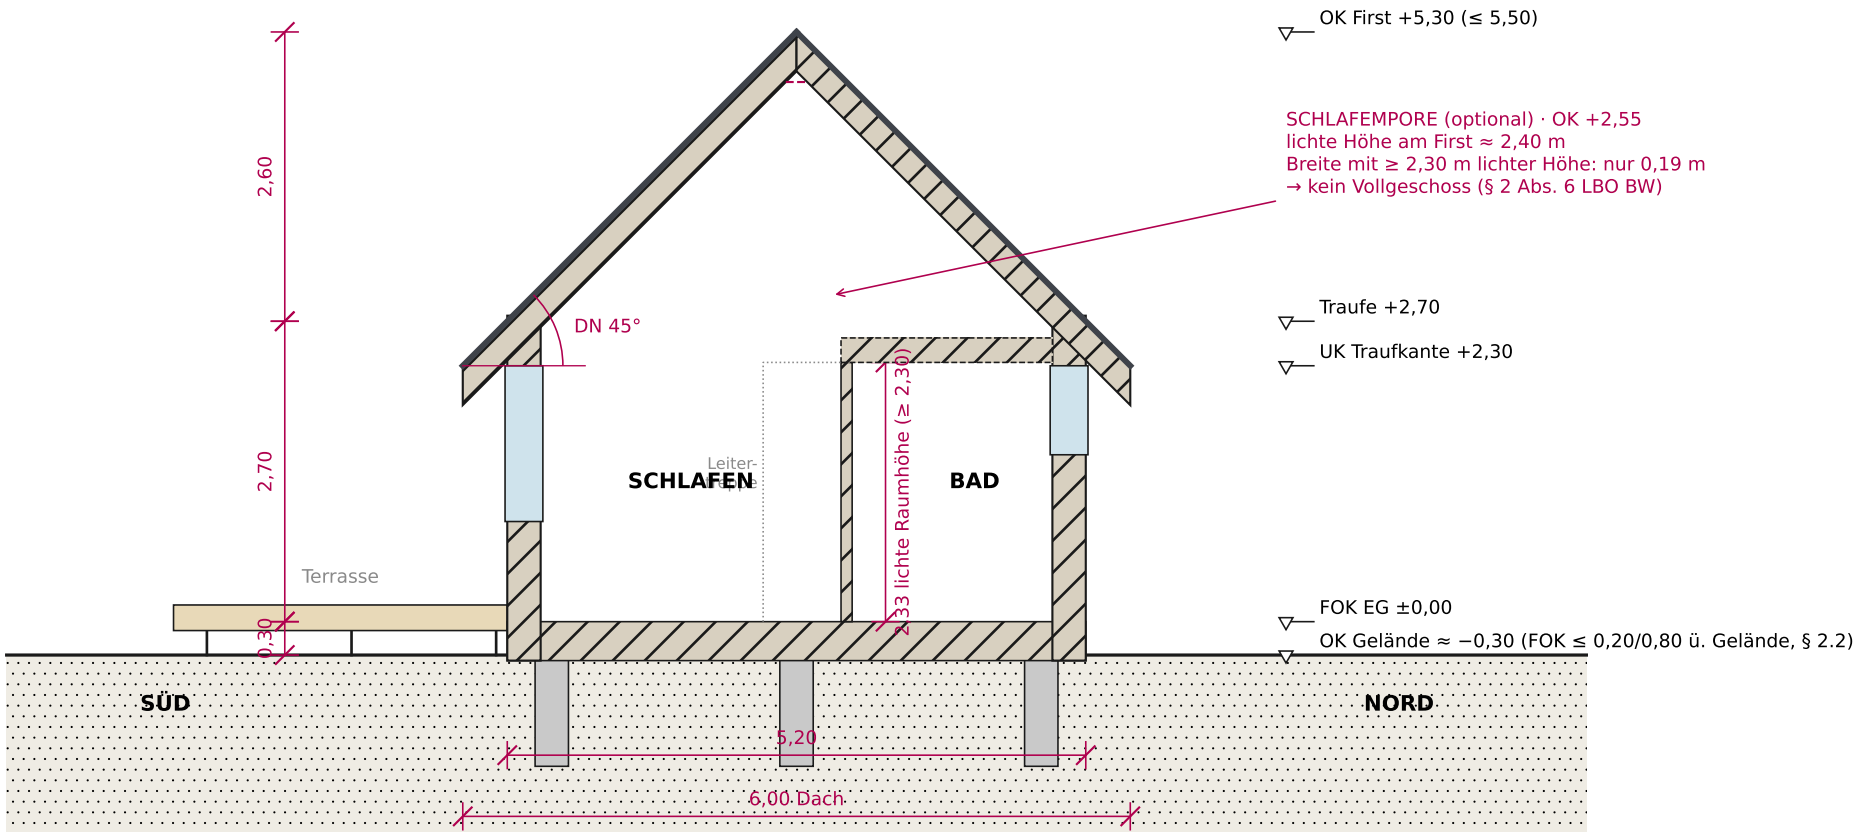

Punkt-/Schraubfundamente, frostfrei; Bodenplatte entfällt (Holzbalkendecke, hinterlüftet)

Dachaufbau (von außen)

Stehfalzdeckung, beschichtetes Stahl-/Aluminiumblech, anthrazit

Trennlage, Holzschalung 24 mm, Hinterlüftung 40 mm

Unterdeckbahn diffusionsoffen

Sparren 80/240 mit Holzfaser-/Zellulosedämmung 240 mm

Dampfbremse, Lattung, Innenbekleidung Fichte/Tanne weiß lasiert

optional: extensive Dachbegrünung statt Blech (Hinweis B-Plan)

Außenwand (von außen) ≈ 30 cm

Lärche sägerau 24 mm, horizontal, offene Fuge, unbehandelt (vergraut)

Konterlattung 30 mm, Fassadenbahn

Holzrahmen 60/200 mit Holzfaserdämmung 200 mm

OSB/Dampfbremse, Installationsebene 40 mm, Bekleidung

Boden

Dielen Eiche/Douglasie 25 mm, Holzbalkendecke 240 mm gedämmt

Hinterlüfteter Kriechraum, Punkt-/Schraubfundamente

Haustechnik (Vorschlag)

Kaminofen + Infrarot-/Elektro-Direktheizung (Wochenendnutzung)

Trinkwasser/Abwasser: Anschluss lt. Gemeinde (Trennsystem, Hinweis B-Plan)

Regenwasser → Zisterne ≥ 3 m³ (Gartenbewässerung)

PV-Module dachintegriert Südseite optional (Blende in Dachfarbe)

Neubau eines Wochenendhauses

Grenzweg 12 · 69245 Bammental · Flurstück 7348

B-Plan „Wochenendhausgebiet – 1. Änderung (Neufassung)“, Gemeinde Bammental, 11.09.2008

Schnitt A-A - Variante A


VORENTWURF · Stand 09/2026 · zur Vorabstimmung mit der Gemeinde

M 1:50

Blatt 5

Schema-Isometrie - Variante A - Bebauung im Baufenster (Regelfall)

Blick von Südwesten. Nur Volumenstudie - Materialwirkung siehe Referenzbilder / Visualisierungen.

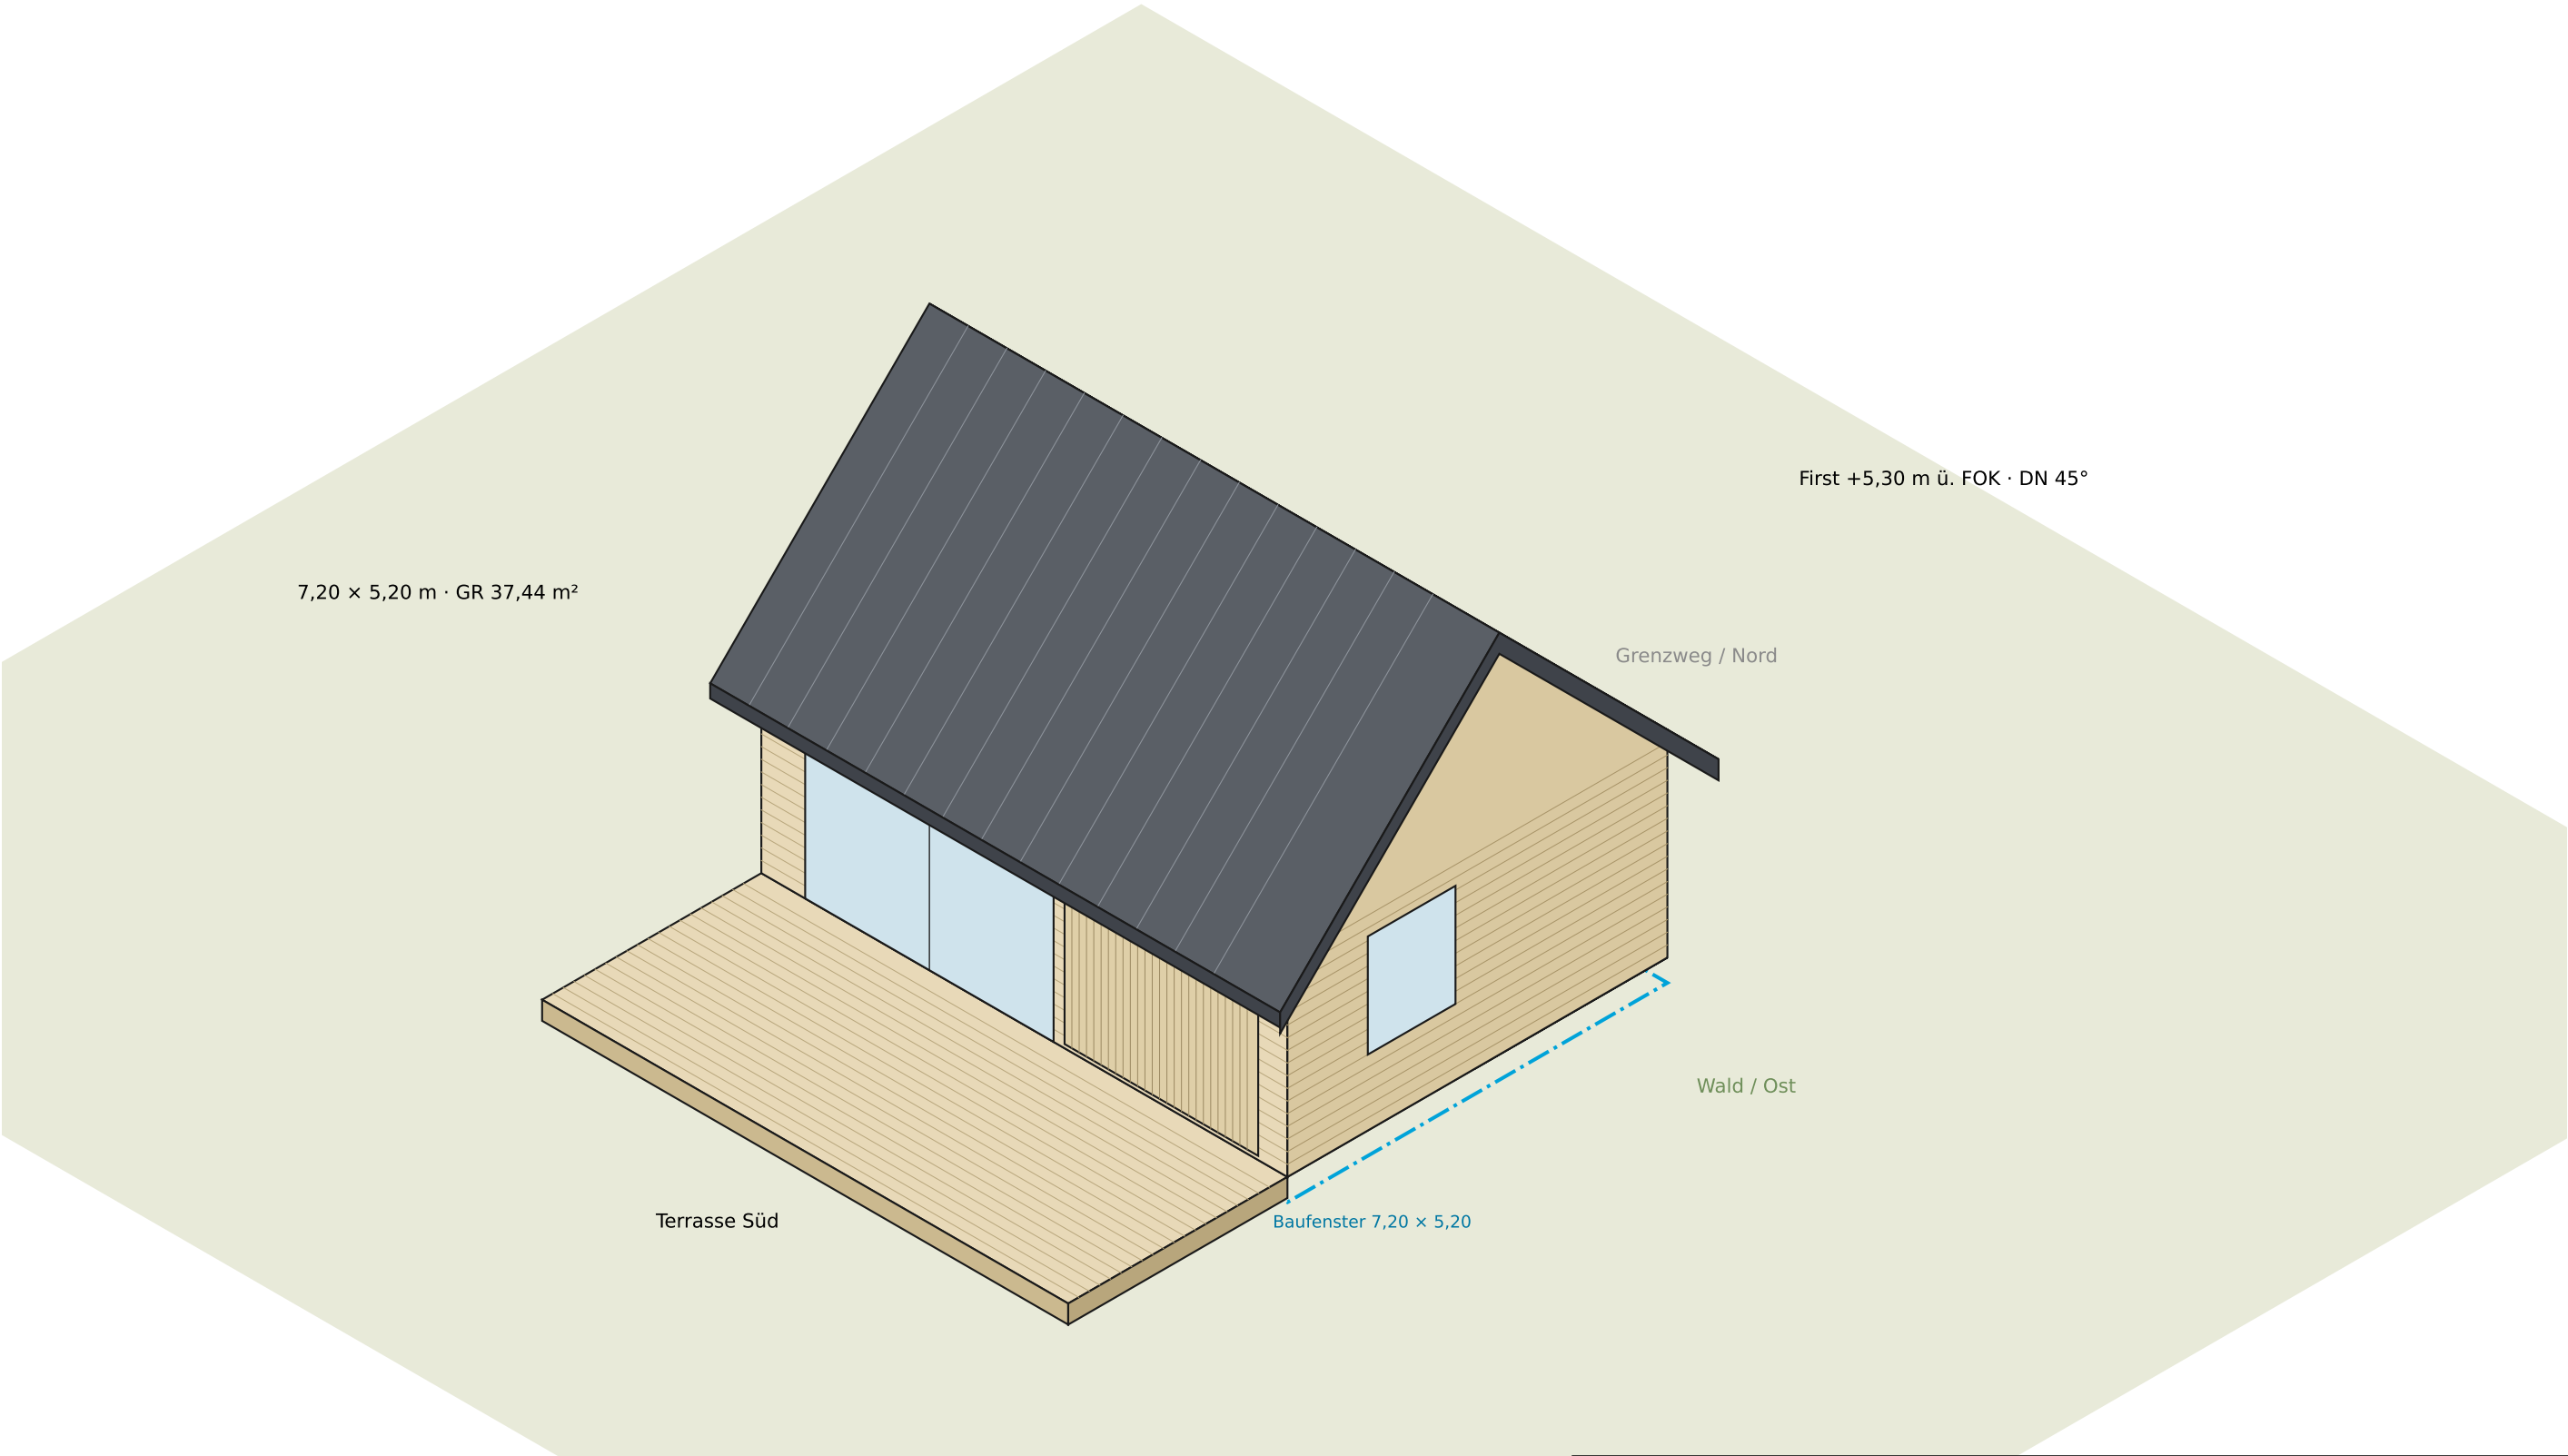

Neubau eines Wochenendhauses

Grenzweg 12 · 69245 Bammental · Flurstück 7348

B-Plan „Wochenendhausgebiet – 1. Änderung (Neufassung)“, Gemeinde Bammental, 11.09.2008


Isometrie - Variante A

VORENTWURF · Stand 09/2026 · zur Vorabstimmung mit der Gemeinde

o. M.

Grundriss Erdgeschoss - Variante B - Überbauung 8,40 × 6,80 m (Antrag auf Befreiung)

Holzrahmenbau, Außenwand 30 cm (inkl. Lärchenschalung), Innenwände 10 cm. Maße in m. Süden = unten (Terrassenseite).

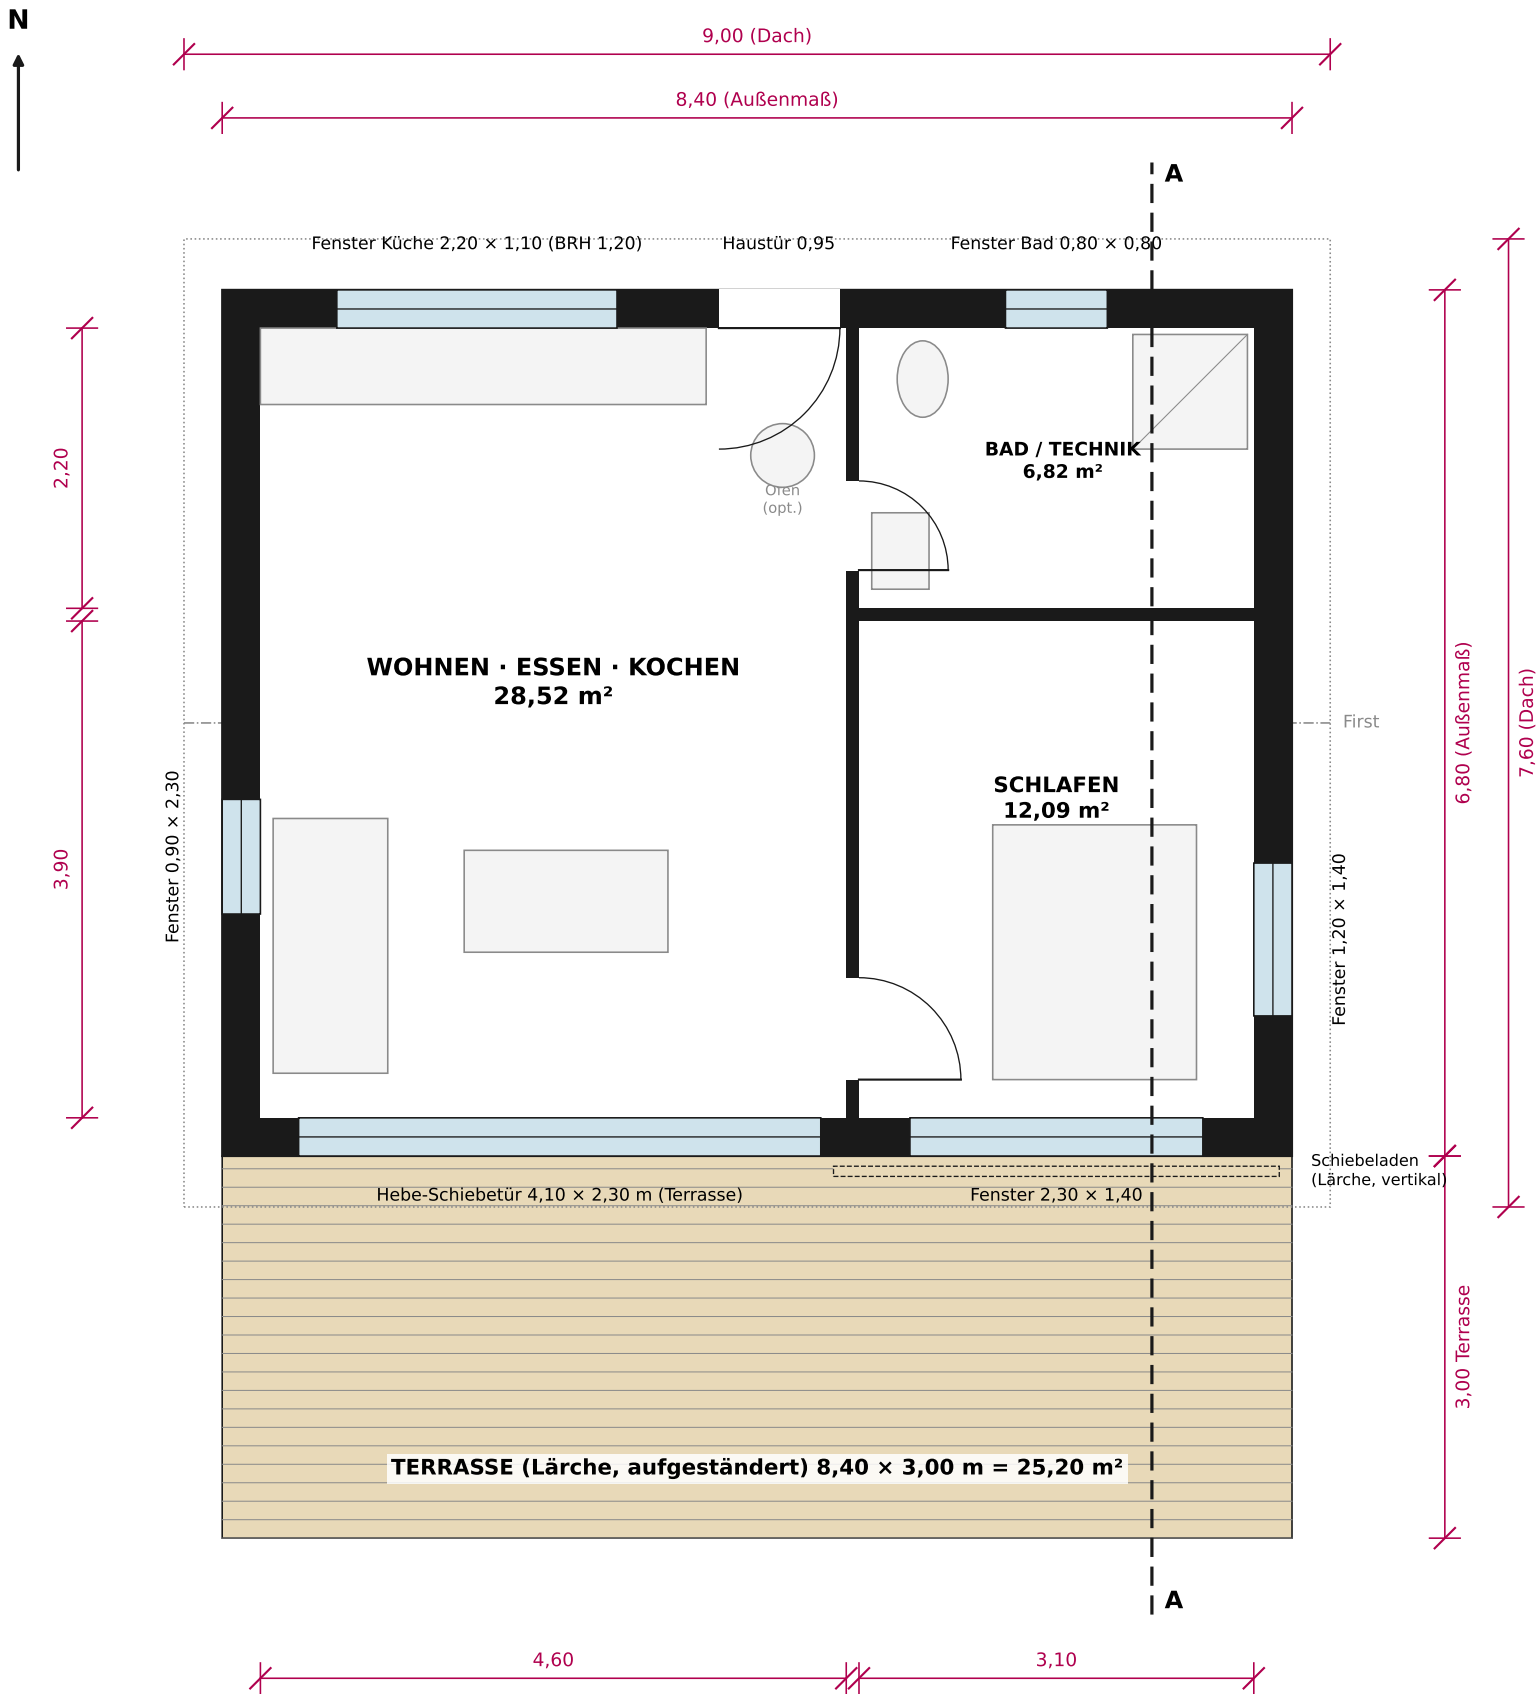

Raumprogramm	
Wohnen / Essen / Kochen	28,52 m²
Schlafen	12,09 m²
Bad / WC / Technik	6,82 m²
Wohnfläche EG netto	47,43 m²
Schlafempore (optional, kein Vollgeschoss)	≈ 19,22 m²
Terrasse (unüberdacht)	25,20 m²

Kennwerte	
Grundfläche GR (Außenmaß)	57,12 m²
Baufenster lt. B-Plan	37,44 m²
GR max. lt. Nutzungsschablone	65,00 m²
Vollgeschosse	I
Bauweise	offen (o)
Traufhöhe (Schnittpunkt Wand/Dach) ü. FOK	2,60 m
Firsthöhe ü. FOK EG (max. 5,50)	5,26 m
Dachneigung / Dachform	38° Satteldach
Dachüberstand Traufe (max. 0,80)	0,40 m
Dachüberstand Ortgang (0,20–0,60)	0,30 m
FOK EG über Gelände (bergs. ≤0,20 / tals. ≤0,80)	≈ 0,20–0,30 m

- Konstruktion**
- Holzrahmenbau, vorgefertigt, diffusionsoffen
 - Fassade: Lärche sägerau, horizontal, unbehandelt
 - Dach: Stehfalz, beschichtetes Blech (kein Cu/Zn/Pb blank)
 - Gründung: Punkt-/Schraubfundamente (minimaler Eingriff)

Neubau eines Wochenendhauses

Grenzweg 12 · 69245 Bammental · Flurstück 7348
B-Plan „Wochenendhausgebiet – 1. Änderung (Neufassung)“, Gemeinde Bammental, 11.09.2008

Grundriss EG - Variante B

VORENTWURF · Stand 09/2026 · zur Vorabstimmung mit der Gemeinde


M 1:50

Blatt 7


Ansichten - Variante B - Überbauung 8,40 x 6,80 m (Antrag auf Befreiung)

Fassade Lärche horizontal (vergraut), Dach Stehfalz anthrazit (beschichtet), Fenster Holz-Alu. Höhen in m bezogen auf FOK EG = ±0,00.


Ansicht Süd (Terrasse / Gartenseite)

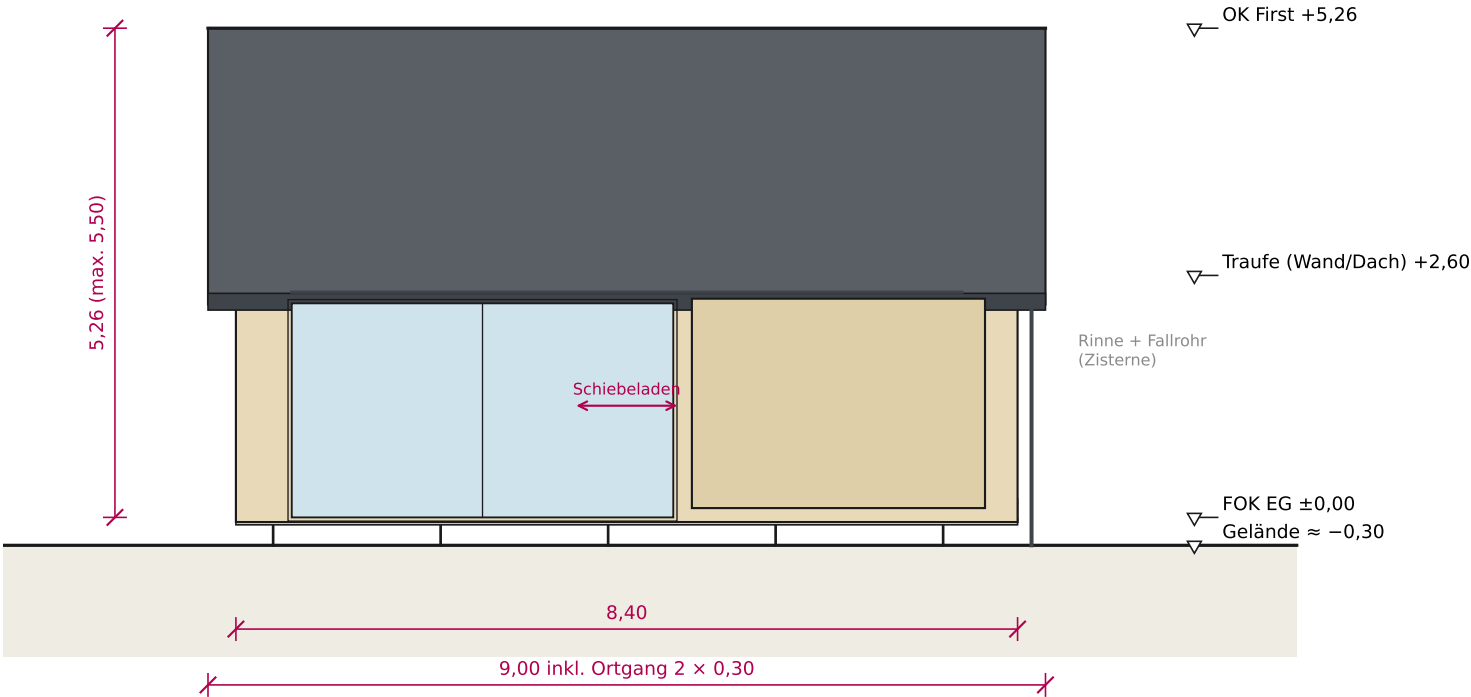


Ansicht Nord (Eingang / Grenzweg)

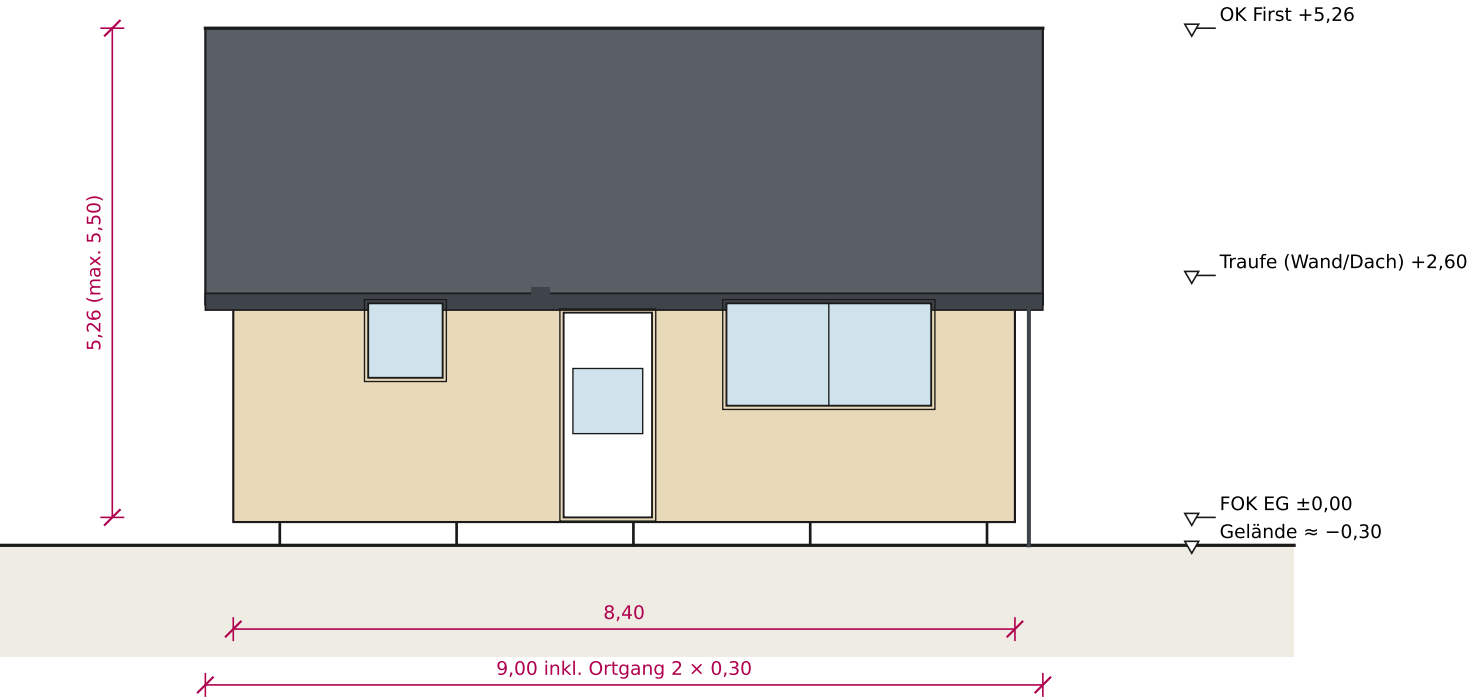

Ansicht Ost (Giebel, Waldseite)

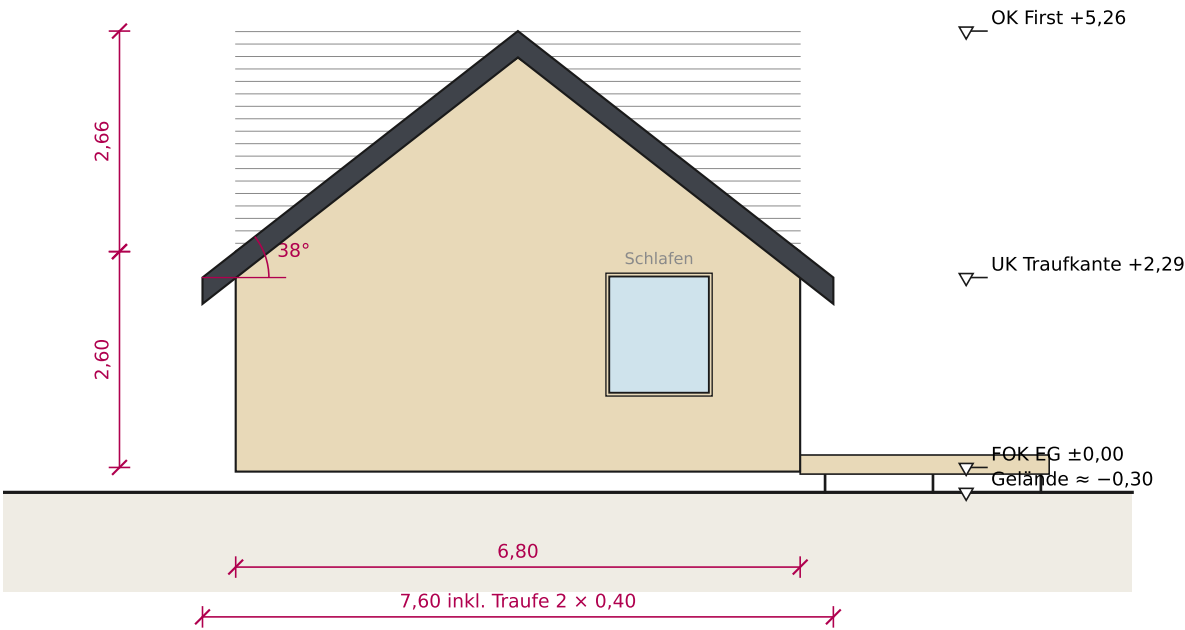

Ansicht West (Giebel)

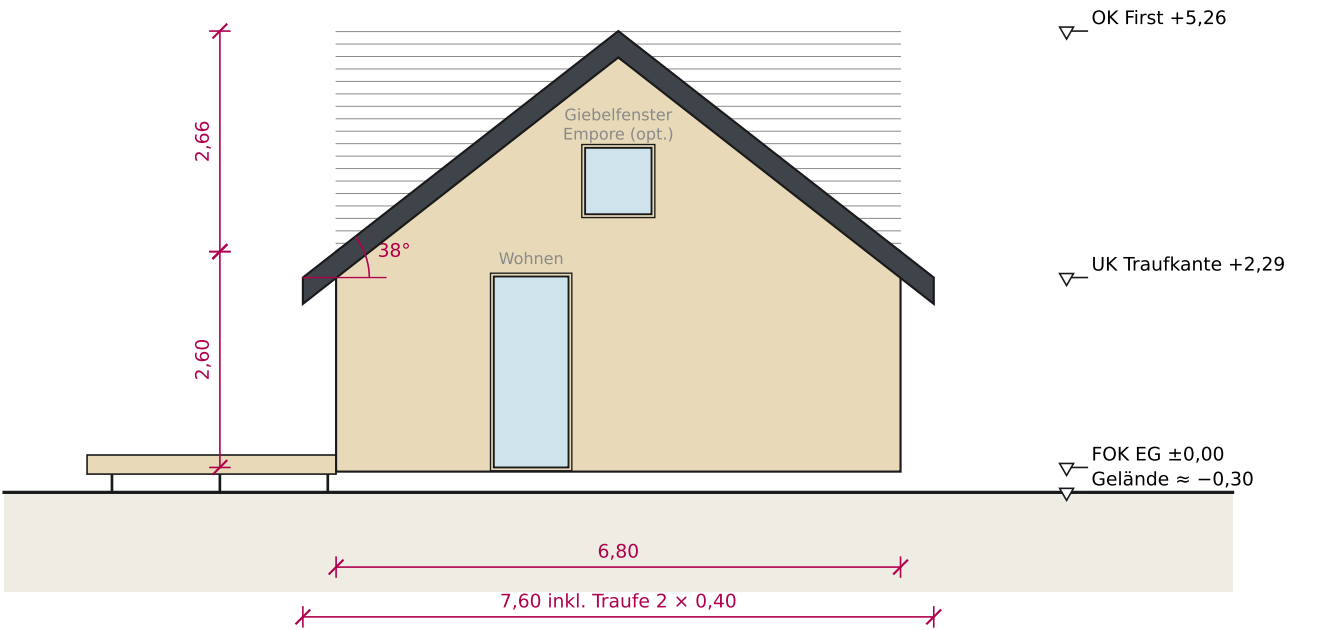

Neubau eines Wochenendhauses

Grenzweg 12 · 69245 Bammental · Flurstück 7348
B-Plan „Wochenendhausgebiet – 1. Änderung (Neufassung)“, Gemeinde Bammental, 11.09.2008

Ansichten - Variante B


VORENTWURF · Stand 09/2026 · zur Vorabstimmung mit der Gemeinde

M 1:100

Blatt 8

Schnitt A-A - Variante B - Überbauung 8,40 x 6,80 m (Antrag auf Befreiung)

Schnitt durch Schlaf-/Badzone mit optionaler Schlafempore (kein Vollgeschoss: lichte Höhe $\geq 2,30$ m auf deutlich $< 3/4$ der Grundfläche).

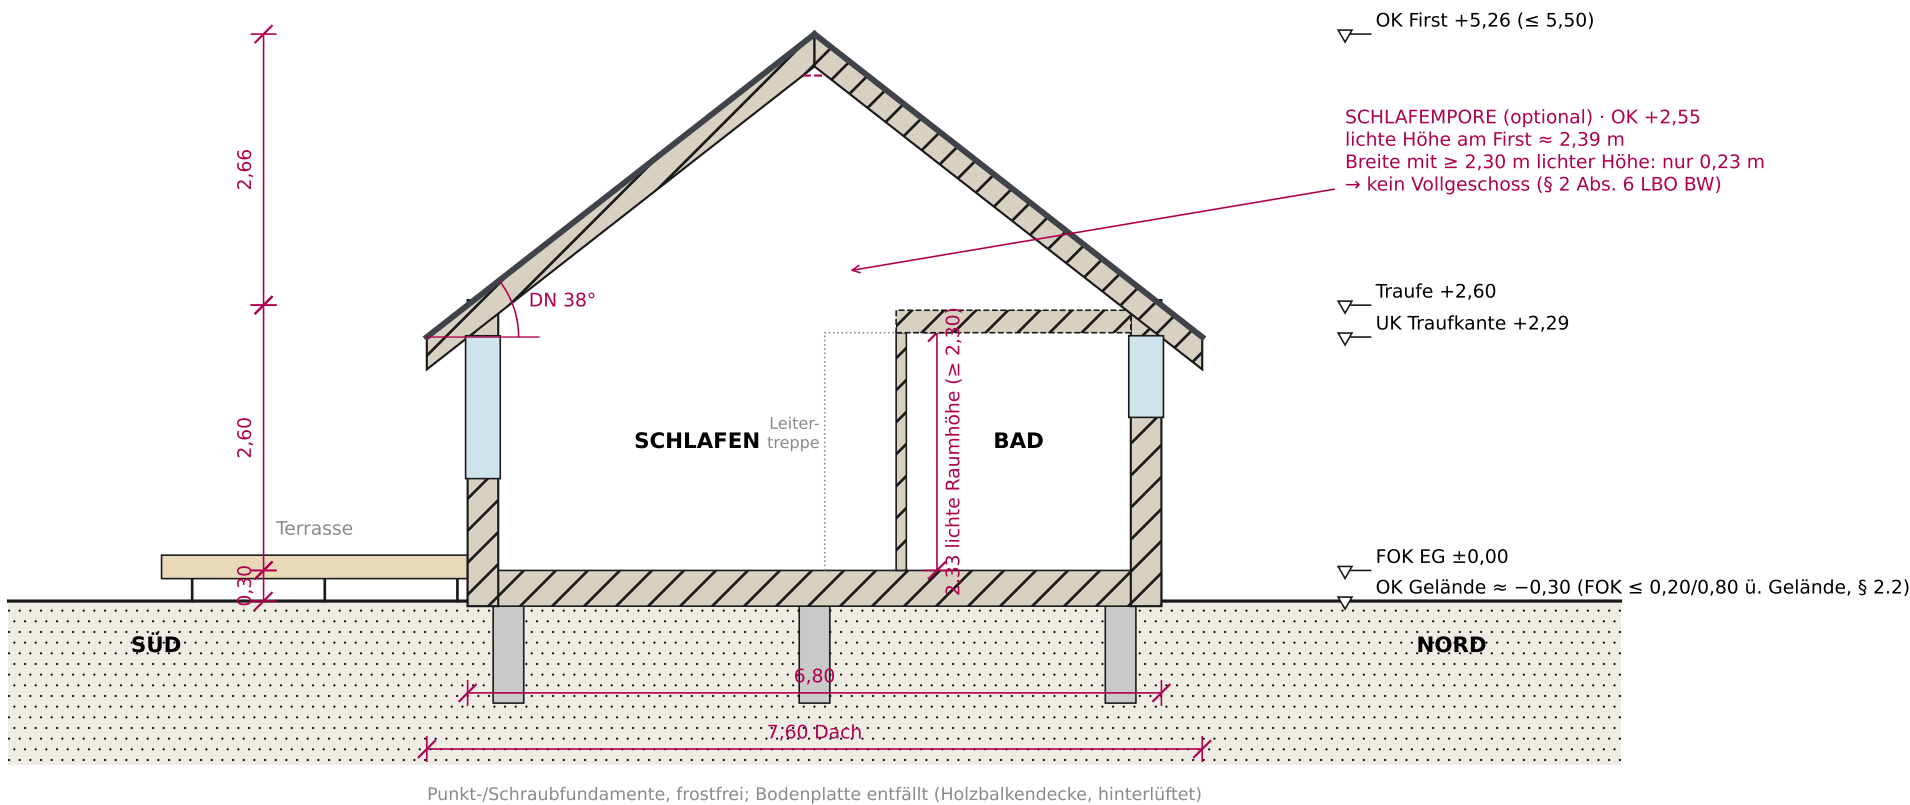

Dachaufbau (von außen)

Stehfalzdeckung, beschichtetes Stahl-/Aluminiumblech, anthrazit

Trennlage, Holzschalung 24 mm, Hinterlüftung 40 mm

Unterdeckbahn diffusionsoffen

Sparren 80/240 mit Holzfaser-/Zellulosedämmung 240 mm

Dampfbremse, Lattung, Innenbekleidung Fichte/Tanne weiß lasiert

optional: extensive Dachbegrünung statt Blech (Hinweis B-Plan)

Außenwand (von außen) ≈ 30 cm

Lärche sägerau 24 mm, horizontal, offene Fuge, unbehandelt (vergraut)

Konterlattung 30 mm, Fassadenbahn

Holzrahmen 60/200 mit Holzfaserdämmung 200 mm

OSB/Dampfbremse, Installationsebene 40 mm, Bekleidung

Boden

Dielen Eiche/Douglasie 25 mm, Holzbalkendecke 240 mm gedämmt

Hinterlüfteter Kriechraum, Punkt-/Schraubfundamente

Haustechnik (Vorschlag)

Kaminofen + Infrarot-/Elektro-Direktheizung (Wochenendnutzung)

Trinkwasser/Abwasser: Anschluss lt. Gemeinde (Trennsystem, Hinweis B-Plan)

Regenwasser → Zisterne ≥ 3 m³ (Gartenbewässerung)

PV-Module dachintegriert Südseite optional (Blende in Dachfarbe)

Neubau eines Wochenendhauses

Grenzweg 12 · 69245 Bammental · Flurstück 7348

B-Plan „Wochenendhausgebiet – 1. Änderung (Neufassung)“, Gemeinde Bammental, 11.09.2008

Schnitt A-A - Variante B


VORENTWURF · Stand 09/2026 · zur Vorabstimmung mit der Gemeinde

M 1:50

Blatt 9

Schema-Isometrie - Variante B - Überbauung 8,40 × 6,80 m (Antrag auf Befreiung)

Blick von Südwesten. Nur Volumenstudie – Materialwirkung siehe Referenzbilder / Visualisierungen.

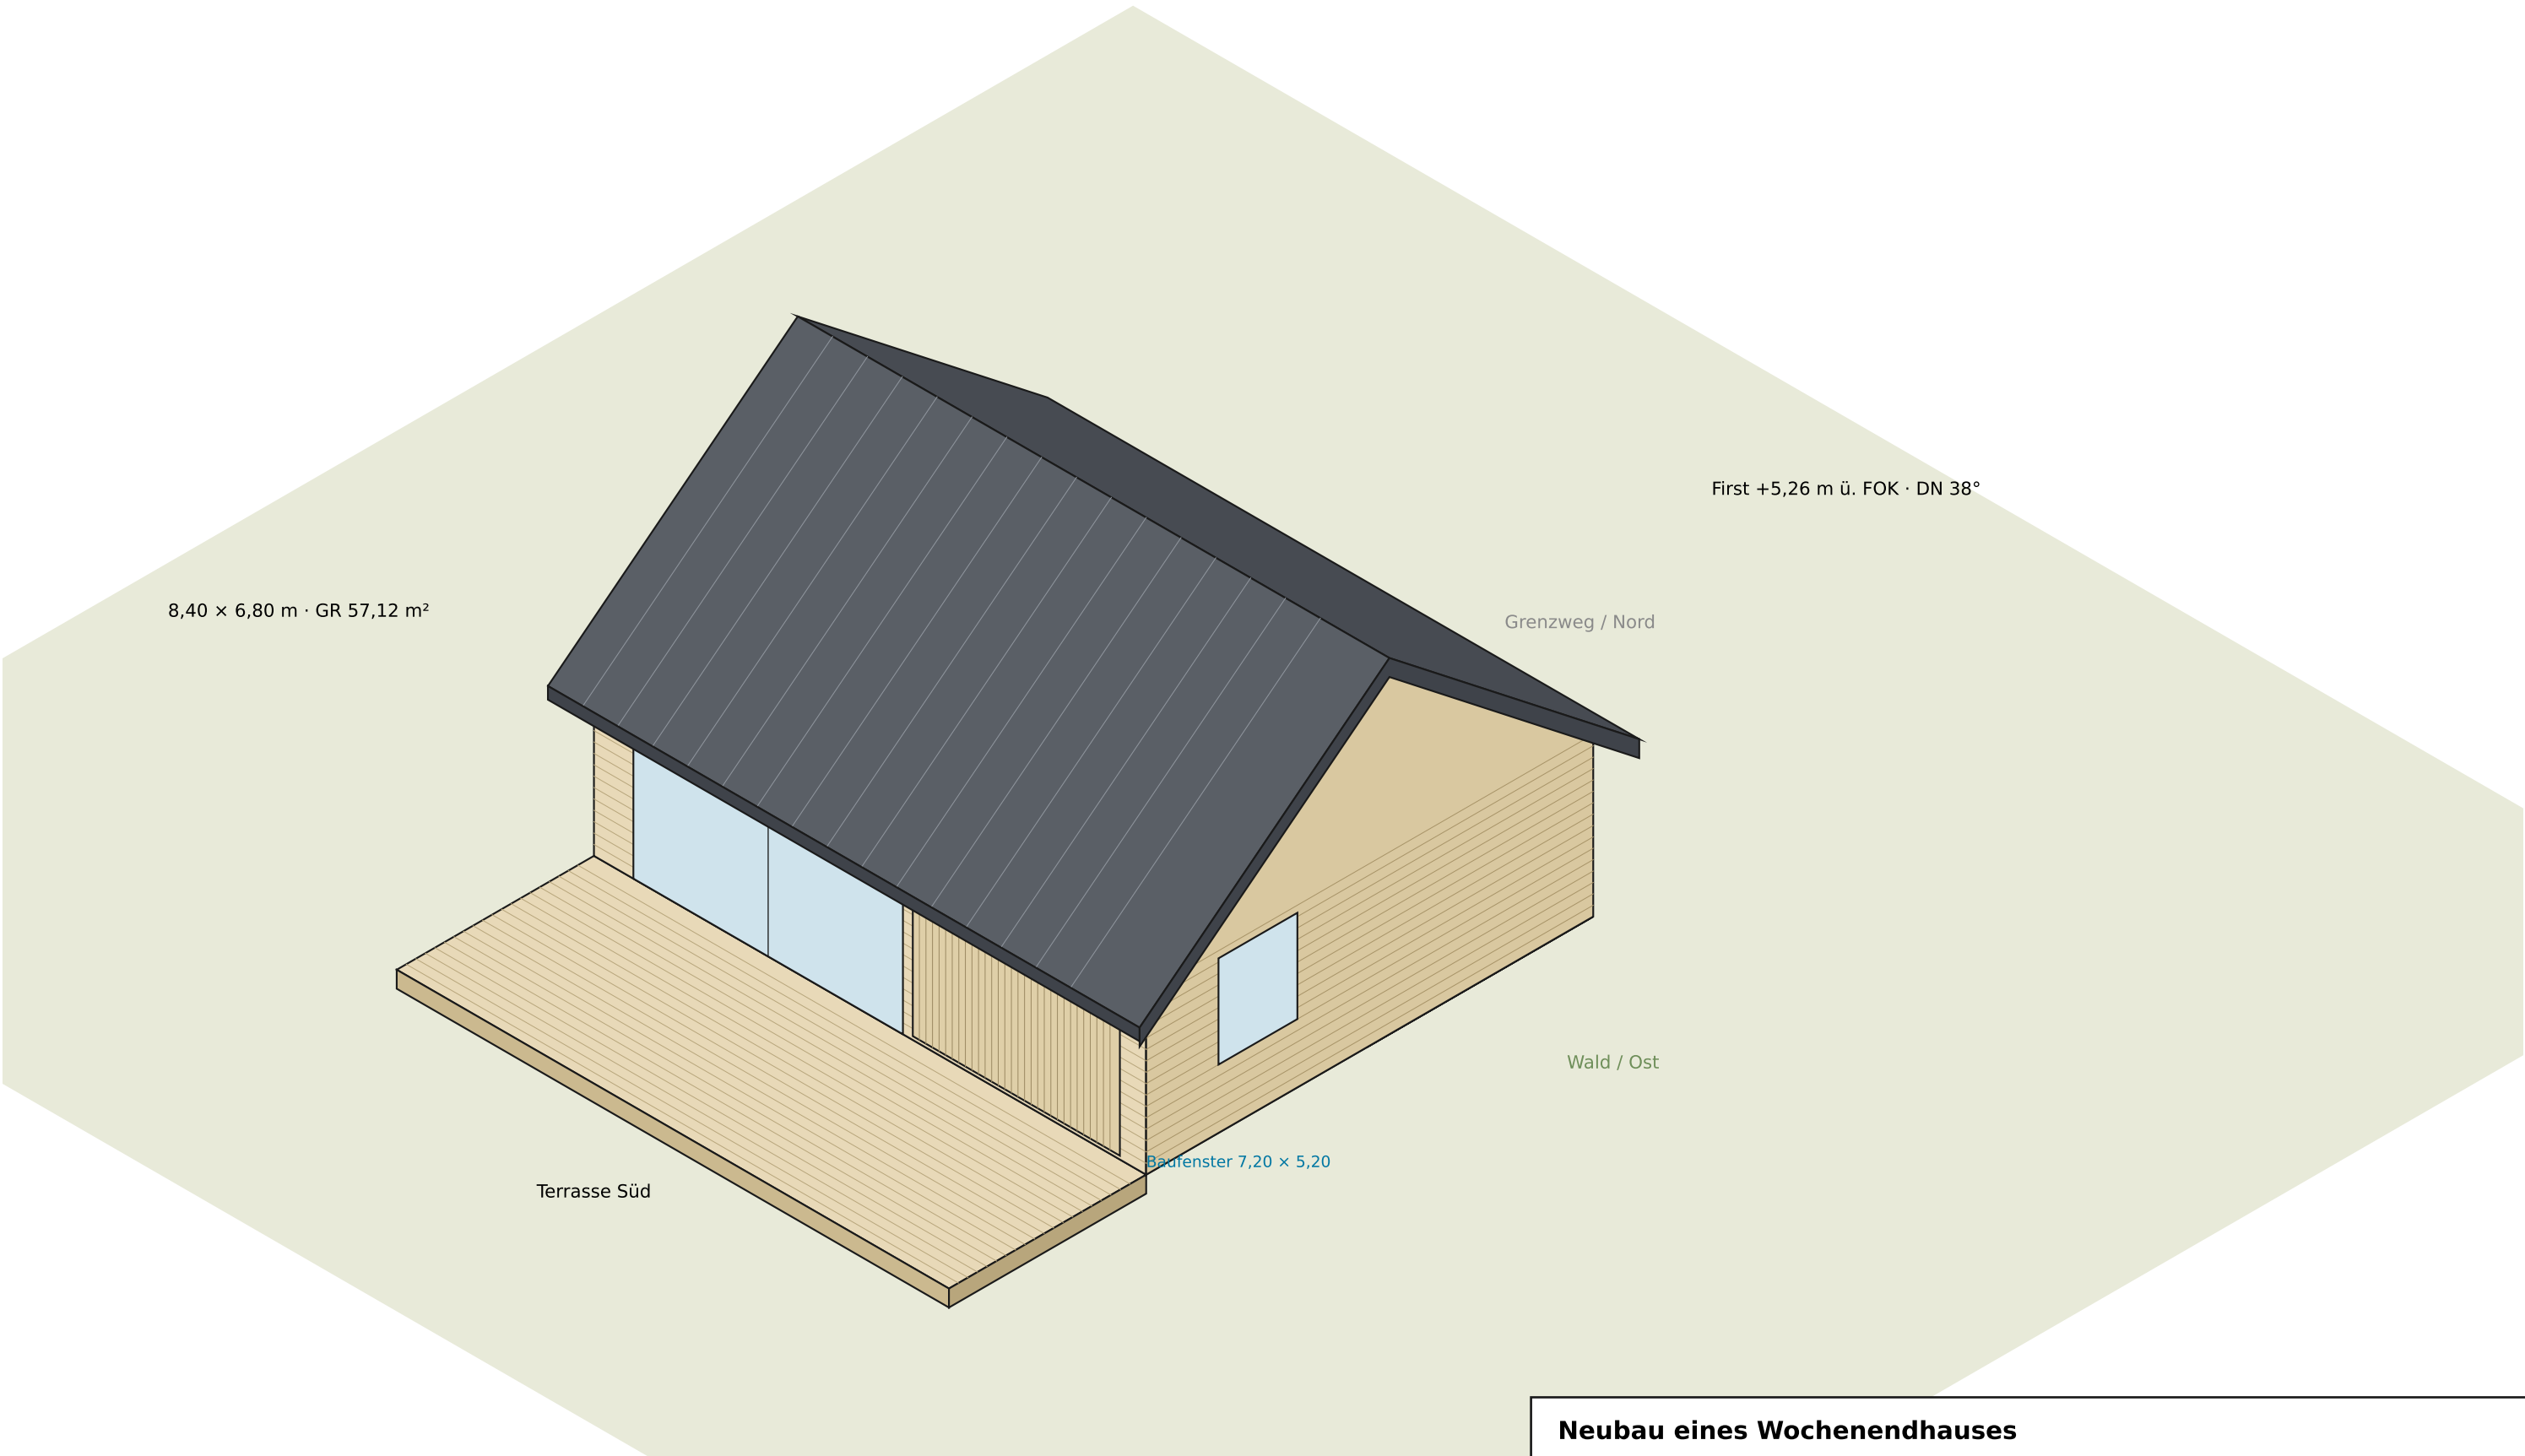

Neubau eines Wochenendhauses

Grenzweg 12 · 69245 Bammental · Flurstück 7348
B-Plan „Wochenendhausgebiet – 1. Änderung (Neufassung)“, Gemeinde Bammental, 11.09.2008

Isometrie - Variante B

VORENTWURF · Stand 09/2026 · zur Vorabstimmung mit der Gemeinde

Nachweis der planungsrechtlichen Festsetzungen (B-Plan „Wochenendhausgebiet - 1. Änderung“)

Prüfung beider Varianten gegen die textlichen Festsetzungen, die Nutzungsschablone und die örtlichen Bauvorschriften (Dachüberstand).

Nr.	Festsetzung / Vorschrift	Anforderung	Variante A (7,20×5,20)	Variante B (8,40×6,80)
1.1	Art der Nutzung: SO Wochenendhaus	nur Wochenendhäuser	Wochenendhaus, 1 Wohneinheit ✓	Wochenendhaus, 1 Wohneinheit ✓
NS	Grundfläche GR max.	65 m²	37,44 m² ✓ eingehalten	57,12 m² ✓ eingehalten
NS	Zahl der Vollgeschosse	I (max.)	I – Empore kein Vollgeschoss ✓	I – Empore kein Vollgeschoss ✓
NS	Bauweise	offen (o)	Einzelhaus ✓	Einzelhaus ✓
§ 9(1)2	Überbaubare Grundstücksfläche (Baugrenze)	Baufenster 7,20 × 5,20 m	Außenkante = Baugrenze ✓ (Dachüberstand als untergeordnetes Bauteil, § 23 (3) BauNVO)	✗ Befreiung § 31 (2) BauGB erforderlich – Überschreitung 0,60 m je Seite (Traufe) / 0,80 m je Seite (Ortgang), begründet s. Bericht
2.1	GRZ inkl. Nebenanlagen (Terrasse, Stellplatz, Zufahrt)	≤ 0,15	≈ 0,09 bei 900 m² ✓	≈ 0,12 bei 900 m² ✓
2.2	FOK EG über urspr. Gelände	bergseits ≤ 0,20 m, talseits ≤ 0,80 m	≈ 0,20–0,30 m (Geländeaufmaß erforderlich) ✓	≈ 0,20–0,30 m ✓
2.3	Firsthöhe ab FOK EG	≤ 5,50 m	5,30 m ✓	5,26 m ✓
3	Abstand zu seitr. Grenzen (nur in Flächen [1])	≥ 5,0 m	Baufenster 7348 nicht mit [1] gekennzeichnet; LBO-Abstand ≥ 2,5 m ✓ (ca. 4 m Ost)	≈ 3,4 m Ost ✓ (LBO)
4	Mindestgröße Baugrundstück	900 m²	Fläche lt. Kataster nachweisen	Fläche lt. Kataster nachweisen
5.1	Terrasse	gesamte Gebäudebreite, Tiefe ≤ 6,0 m	7,20 × 3,00 m ✓	8,40 × 3,00 m ✓
5.2	Garagen/Carports/überdachte Sitzplätze	nur im Baufenster	keine (offener Stellplatz) ✓	keine ✓
7.1	Dachflächen	kein unbeschichtetes Cu/Zn/Pb	Stehfalz beschichtet (Stahl/Alu) ✓ – alternativ Gründach	wie A ✓
7.2	Stellplätze, Fußwege	wasserdurchlässig	Schotterrasen / Kiesweg ✓	wie A ✓
9	Baumbestand außerhalb Baufenster	erhalten	Erhalt; Neubau auf Wiese ✓	wie A ✓
öBV § 3	Dachüberstand Traufe / Ortgang	≤ 0,80 m / 0,20–0,60 m	0,40 m / 0,30 m ✓	0,40 m / 0,30 m ✓
Hinw.	Dachbegrünung / Zisterne	empfohlen; ≥ 0,02 m³/m² Dach	Zisterne ≥ 1,0 m³ → 3 m³ vorgesehen ✓	≥ 1,4 m³ → 3 m³ ✓
Hinw.	Artenschutz	Brutstätten/Orchideen prüfen	Bauen auf Wiese, keine Fällung; Vorprüfung Fachbüro	wie A
LBO § 4(3)	Waldabstand 30 m	Ausnahme durch Baurechtsbehörde im Benehmen mit Forst	Baufenster liegt lt. B-Plan im Streifen → Ausnahme beantragen	wie A

NS = Nutzungsschablone · öBV = örtliche Bauvorschriften zum B-Plan · Grundstücksfläche und Geländehöhen sind vor Einreichung durch Vermessung zu belegen.

Neubau eines Wochenendhauses

Grenzweg 12 · 69245 Bammental · Flurstück 7348

B-Plan „Wochenendhausgebiet – 1. Änderung (Neufassung)“, Gemeinde Bammental, 11.09.2008

Nachweis Festsetzungen A / B

VORENTWURF · Stand 09/2026 · zur Vorabstimmung mit der Gemeinde

Gestaltung, Material, Einfügung in die Umgebung

Einfügung (§ 34 BauGB-Gedanke / Ortsbild)

- Satteldach wie die bestehenden Wochenendhäuser im Gebiet; First parallel zur langen Gebäudeseite (Ost-West).
- Kleinmaßstäblicher, eingeschossiger Baukörper unter 5,50 m Firsthöhe; keine Dachaufbauten, keine Gauben, keine Dachterrasse.
- Farbigkeit aus der Umgebung: silbergrau vergrautes Holz + dunkles Dach = Farbtöne von Baumrinde, Schatten und Waldboden. Keine weißen Putzflächen, keine glänzenden Oberflächen.
- Geschlossene, ruhige Nordfassade zum Grenzweg mit nur Haustür und zwei kleinen Fenstern; die große Verglasung öffnet sich allein nach Süden zur eigenen Wiese.
- Bauen auf der bestehenden Wiese, keine Fällungen; Terrasse und Wege aufgeständert bzw. wasserdurchlässig.

Material & Farben

- Fassade: Lärche (europ.), sägerau, horizontale Schalung mit offener Fuge ca. 15 cm, unbehandelt → vergraut in 2–3 Jahren gleichmäßig (Referenz: Cabin-Bilder).
- Dach: Doppelstehfalz aus beschichtetem Stahl- oder Aluminiumblech (z. B. Prefa, Farbton anthrazit-grau matt, ca. RAL 7016/7022). Unbeschichtetes Zink/Kupfer/Blei ist gem. 7.1 unzulässig und daher nicht vorgesehen. Alternative: extensives Gründach.
- Fenster: Holz-Alu, außen anthrazit, innen Fichte natur; Hebe-Schiebetür 3-fach verglast, Süd.
- Schiebeladen: Lärche vertikal auf oberer Laufschiene – Sonnen-, Einbruch- und Sturmschutz bei Abwesenheit (Wochenendnutzung).
- Terrasse: Lärche/Douglasie, aufgeständert auf Stelzlagern/Schraubfundamenten, ca. 3 m tief, ohne Überdachung.
- Außenanlagen: Kiesweg, Schotterrasen-Stellplatz, Zisterne 3 m³, Wildwiese belassen, ggf. Obstbaumpflanzung.

Nachhaltigkeit / Technik

- Vorgefertigter Holzrahmenbau (kurze Bauzeit, geringe Belastung des Waldrands), Holzfaserdämmung, diffusionsoffen.
- Punkt-/Schraubfundamente statt Bodenplatte – minimaler Bodeneingriff, rückbaubar.
- Regenwasserrückhalt (Zisterne) gem. Hinweis im B-Plan; optionale PV-Module dachintegriert, matt, in Dachfarbe.
- Beheizung Wochenendnutzung: Kaminofen + elektrische Direktheizung; keine Öl-/Gastanks.

Für das Gespräch mit der Gemeinde – offene Punkte

- 1. Bestätigung, dass Dachüberstände nach örtlicher Bauvorschrift (Traufe ≤ 0,80 m, Ortgang 0,20–0,60 m) über die Baugrenze hinausragen dürfen (untergeordnete Bauteile).
- 2. Haltung der Gemeinde zu Variante B (Befreiung Baugrenze bei Einhaltung GRmax 65 m²); gemeindliches Einvernehmen § 36 BauGB.
- 3. Waldabstand § 4 Abs. 3 LBO: Ausnahme im Benehmen mit dem Forstamt – Baufenster liegt planerisch bereits im 30-m-Streifen.
- 4. Erschließung: Trinkwasser, Abwasser (Trennsystem), Strom; Lage des Hausanschlusses am Grenzweg.
- 5. Artenschutz-Vorprüfung (Vogelbrut, Orchidee Listera ovata) – Zeitfenster für Bauarbeiten.

Neubau eines Wochenendhauses

Grenzweg 12 · 69245 Bammental · Flurstück 7348

B-Plan „Wochenendhausgebiet – 1. Änderung (Neufassung)“, Gemeinde Bammental, 11.09.2008

Gestaltung, Material, Einfügung in die Umgebung

VORENTWURF · Stand 09/2026 · zur Vorabstimmung mit der Gemeinde